

1

94 m²

2



1 A nappaliba lépve a légies étkező lehetővé teszi, hogy átlátható maradjon a tér
2 Különlegessé varázsolja a kanapé mögötti falat a fémkeretbe foglalt élő növényekből álló kompozíció

Szárnyra kelt pillangó

Igenis számít az első benyomás, legyen szó emberekről, de akár egy lakásról is.


Hát így jártam én is, amikor Anikó és Valter először megmutatta a frissen megvásárolt lakásuk alaprajzát.

Szöveg: Petyerák Katalin | Fotó: London Katalin

Talán egy szárnyaszegett pillangóra hasonlított első látásra a sok közlekedővel és a kevés derékszöggel. Tipikus esete annak, hogy leválasztásokkal hogyan lehet egy bérházi lakást úgy átalakítani, hogy a saját tervezője sem ismerne rá. Lehet, ha akkor Anikóból és Valterből nem sugárzott volna az a szeretetteljes optimizmus, talán hozzá sem fogok. Tudták, hogy mit szeretnének kihozni a lakásból. Anikó nagyon igényes, szereti a különleges megoldásokat, és férje, az olasz származású Valter igazi mediterrán lélek egy jó adag romantikával.

Az alaprajz – bevallom – nehezen adta meg magát. Amerikai konyhás nappalit, napfényes hálószobát, egy kisebb dolgozót (ami talán hamarosan gyerekszoba lesz) viszonylag hamar bele lehetett szerkeszteni az alaprajzba, de a vizes és háztartási helyiségeken viszonylag sokáig morfondíroztam.

A konyhaelemeket a tágas nappali szinte elnyelte úgy, hogy bőven maradt tér az étkezésre vagy társas együttlétekre. Mindig gondosan vigyázok arra, ha egy nappaliba építek konyhát, akkor annak a szellőzését és az elszívást is biztosítsam. Azonban itt az elszívó kürtőjét csak komoly átépítések árán lehetett volna a világítóudvarra kiszellőztetni, a ház homlokzatára pedig nem illik újabb csöveket kivezetni. Ekkor jött egy mentő ötlet, hogy a konyhaszigetbe épített alsó kivezetésű elszívót összeköttem a régi konvektor parapet szellőzőjével.

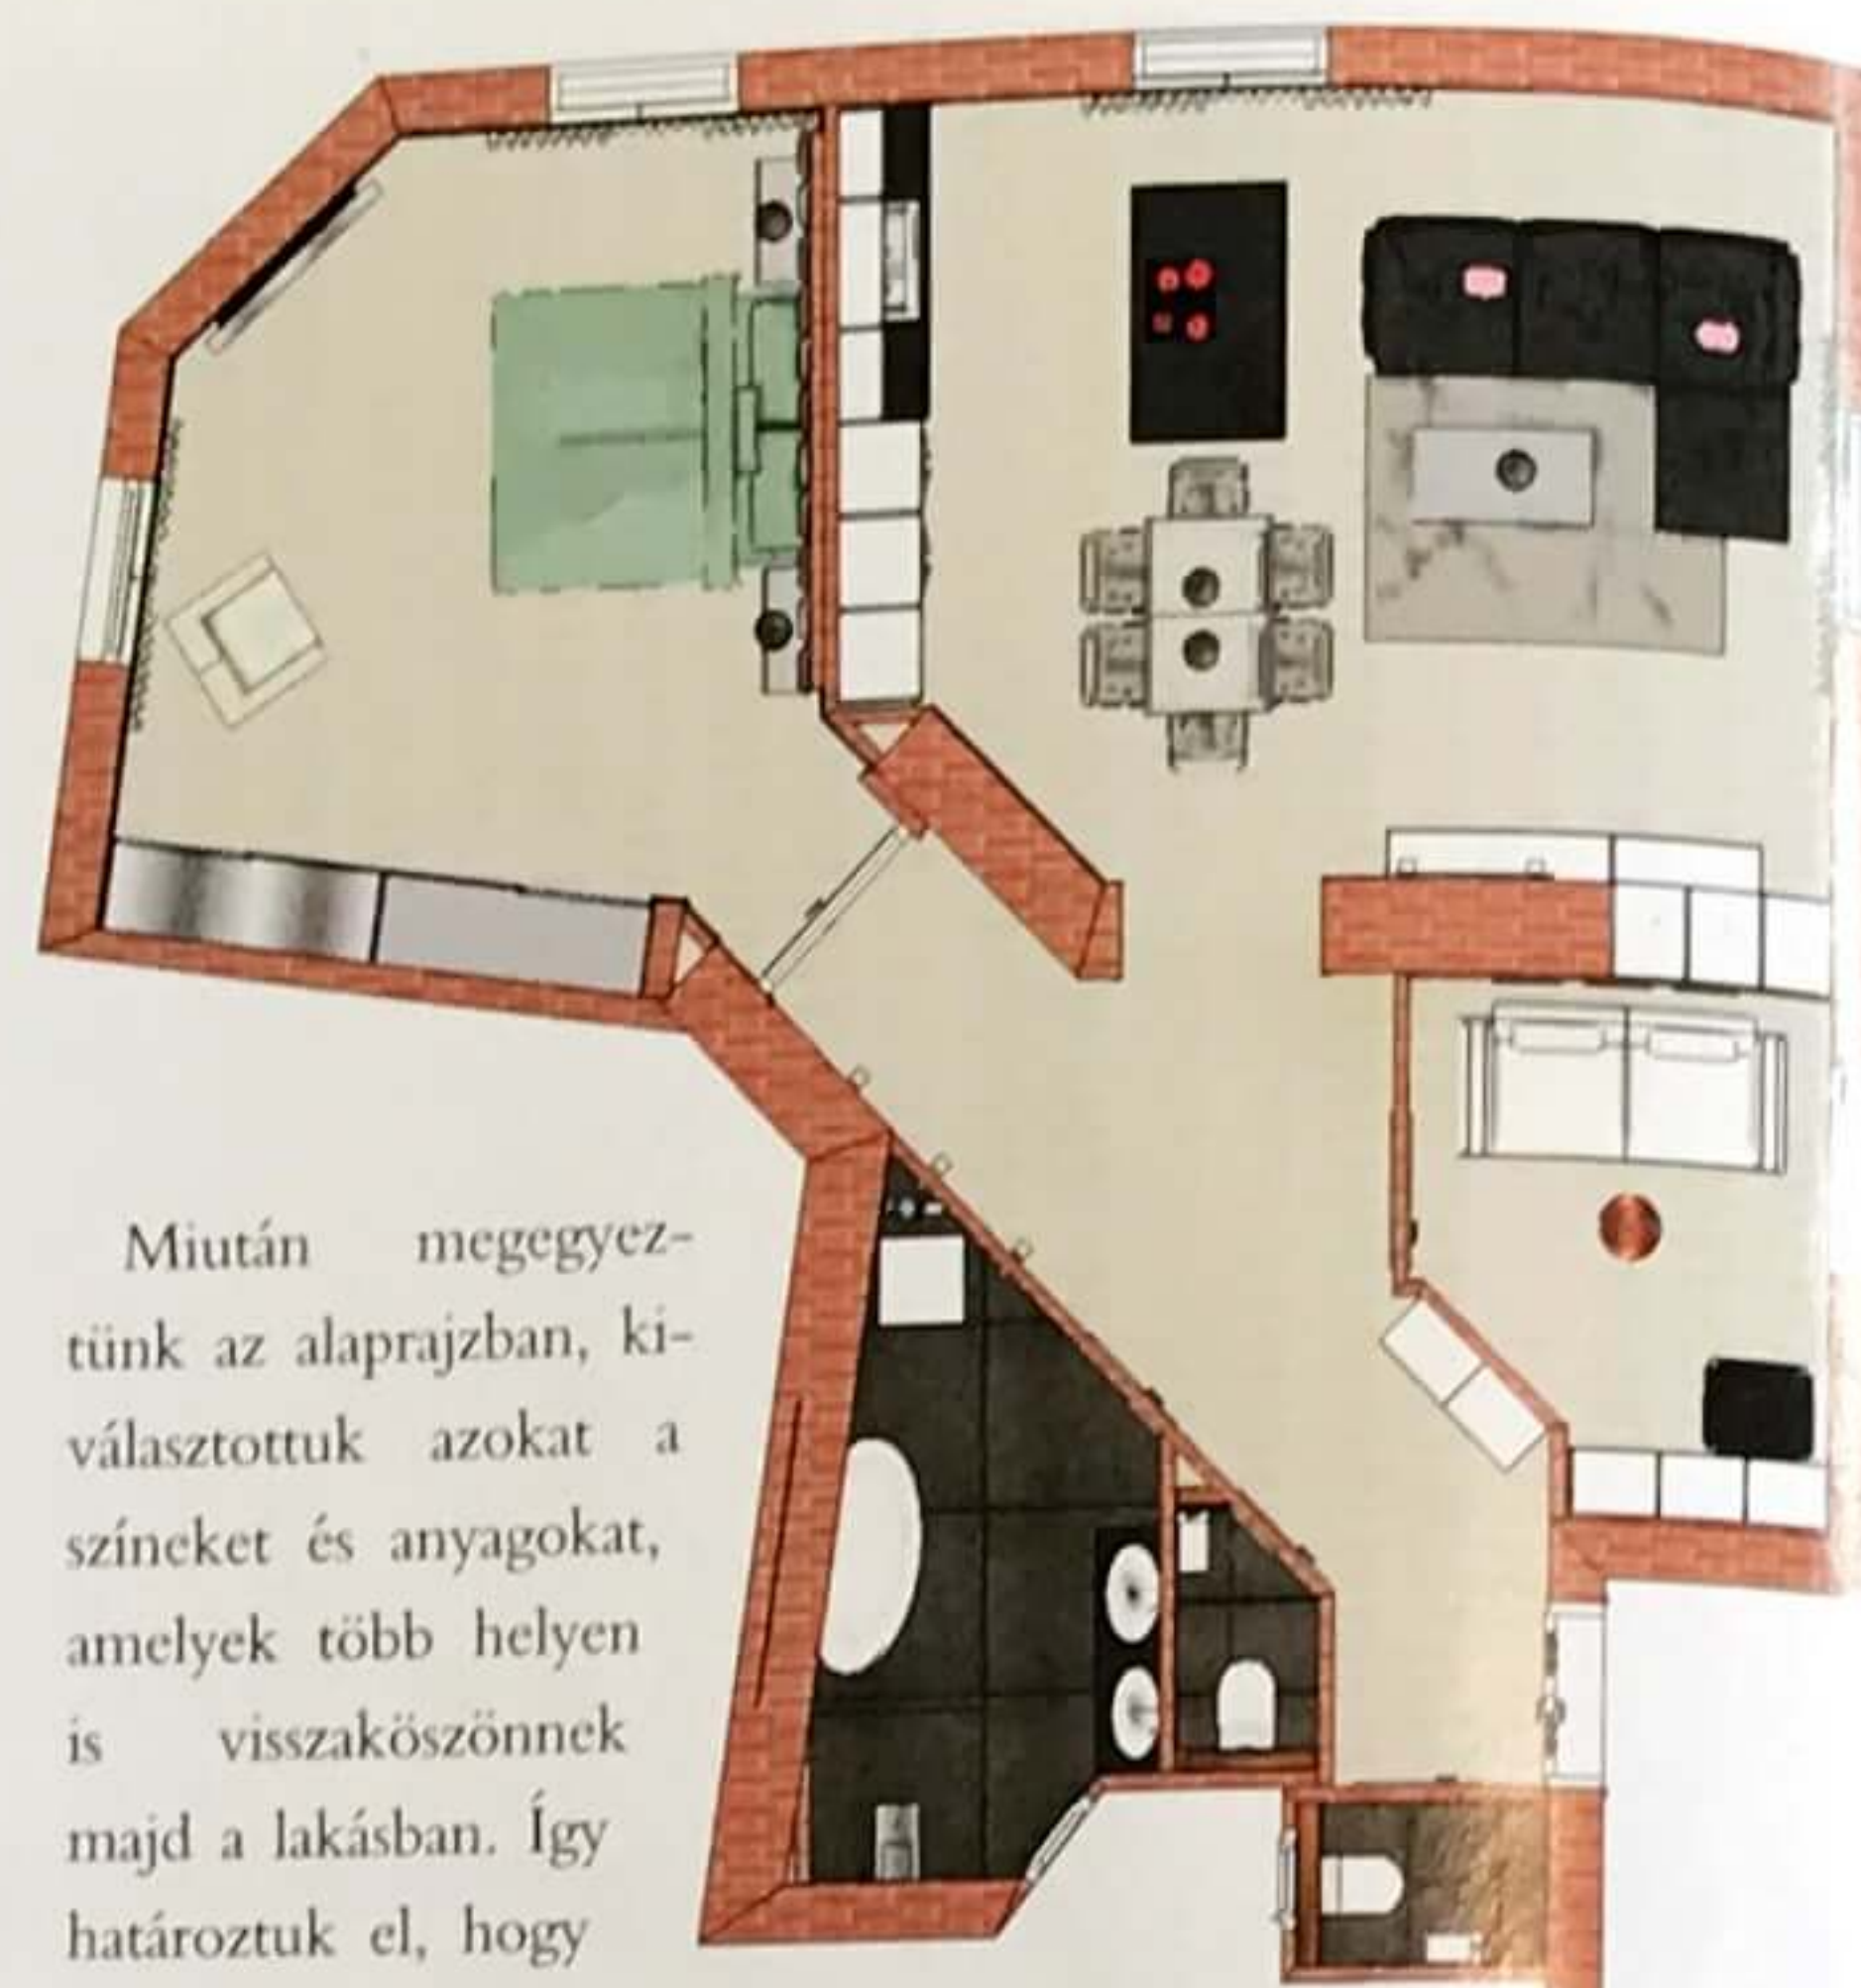

Miután megegyeztünk az alaprajzban, kiválasztottuk azokat a színeket és anyagokat, amelyek több helyen is visszaköszönnek majd a lakásban. Így határoztuk el, hogy a fehér és ezüst-szürke tónusokat halvány rózsaszínnel és Valter kedvencével, az azúrral fogjuk változatossá tenni. A nappaliban a fehér konyhabútort egy spanyol rusztikus, konyak színű, famozaik burkolattal kereteztük. Munkapultnak sötétszürke anyagot választottunk. Ez



3

4




3 Magába rejtli az elszívót és a borhűtőt a konyhasziget. A konyha melletti falat és a konyhaszigetet is Péli Noémi különleges egyedi kerámiái díszítik

4 Porcelanosa Oxford Cognac famozaik hatású burkolat került a tévé mögé. A mellette lévő falmélyedésbe az egyedileg tervezett nappali bútor



5

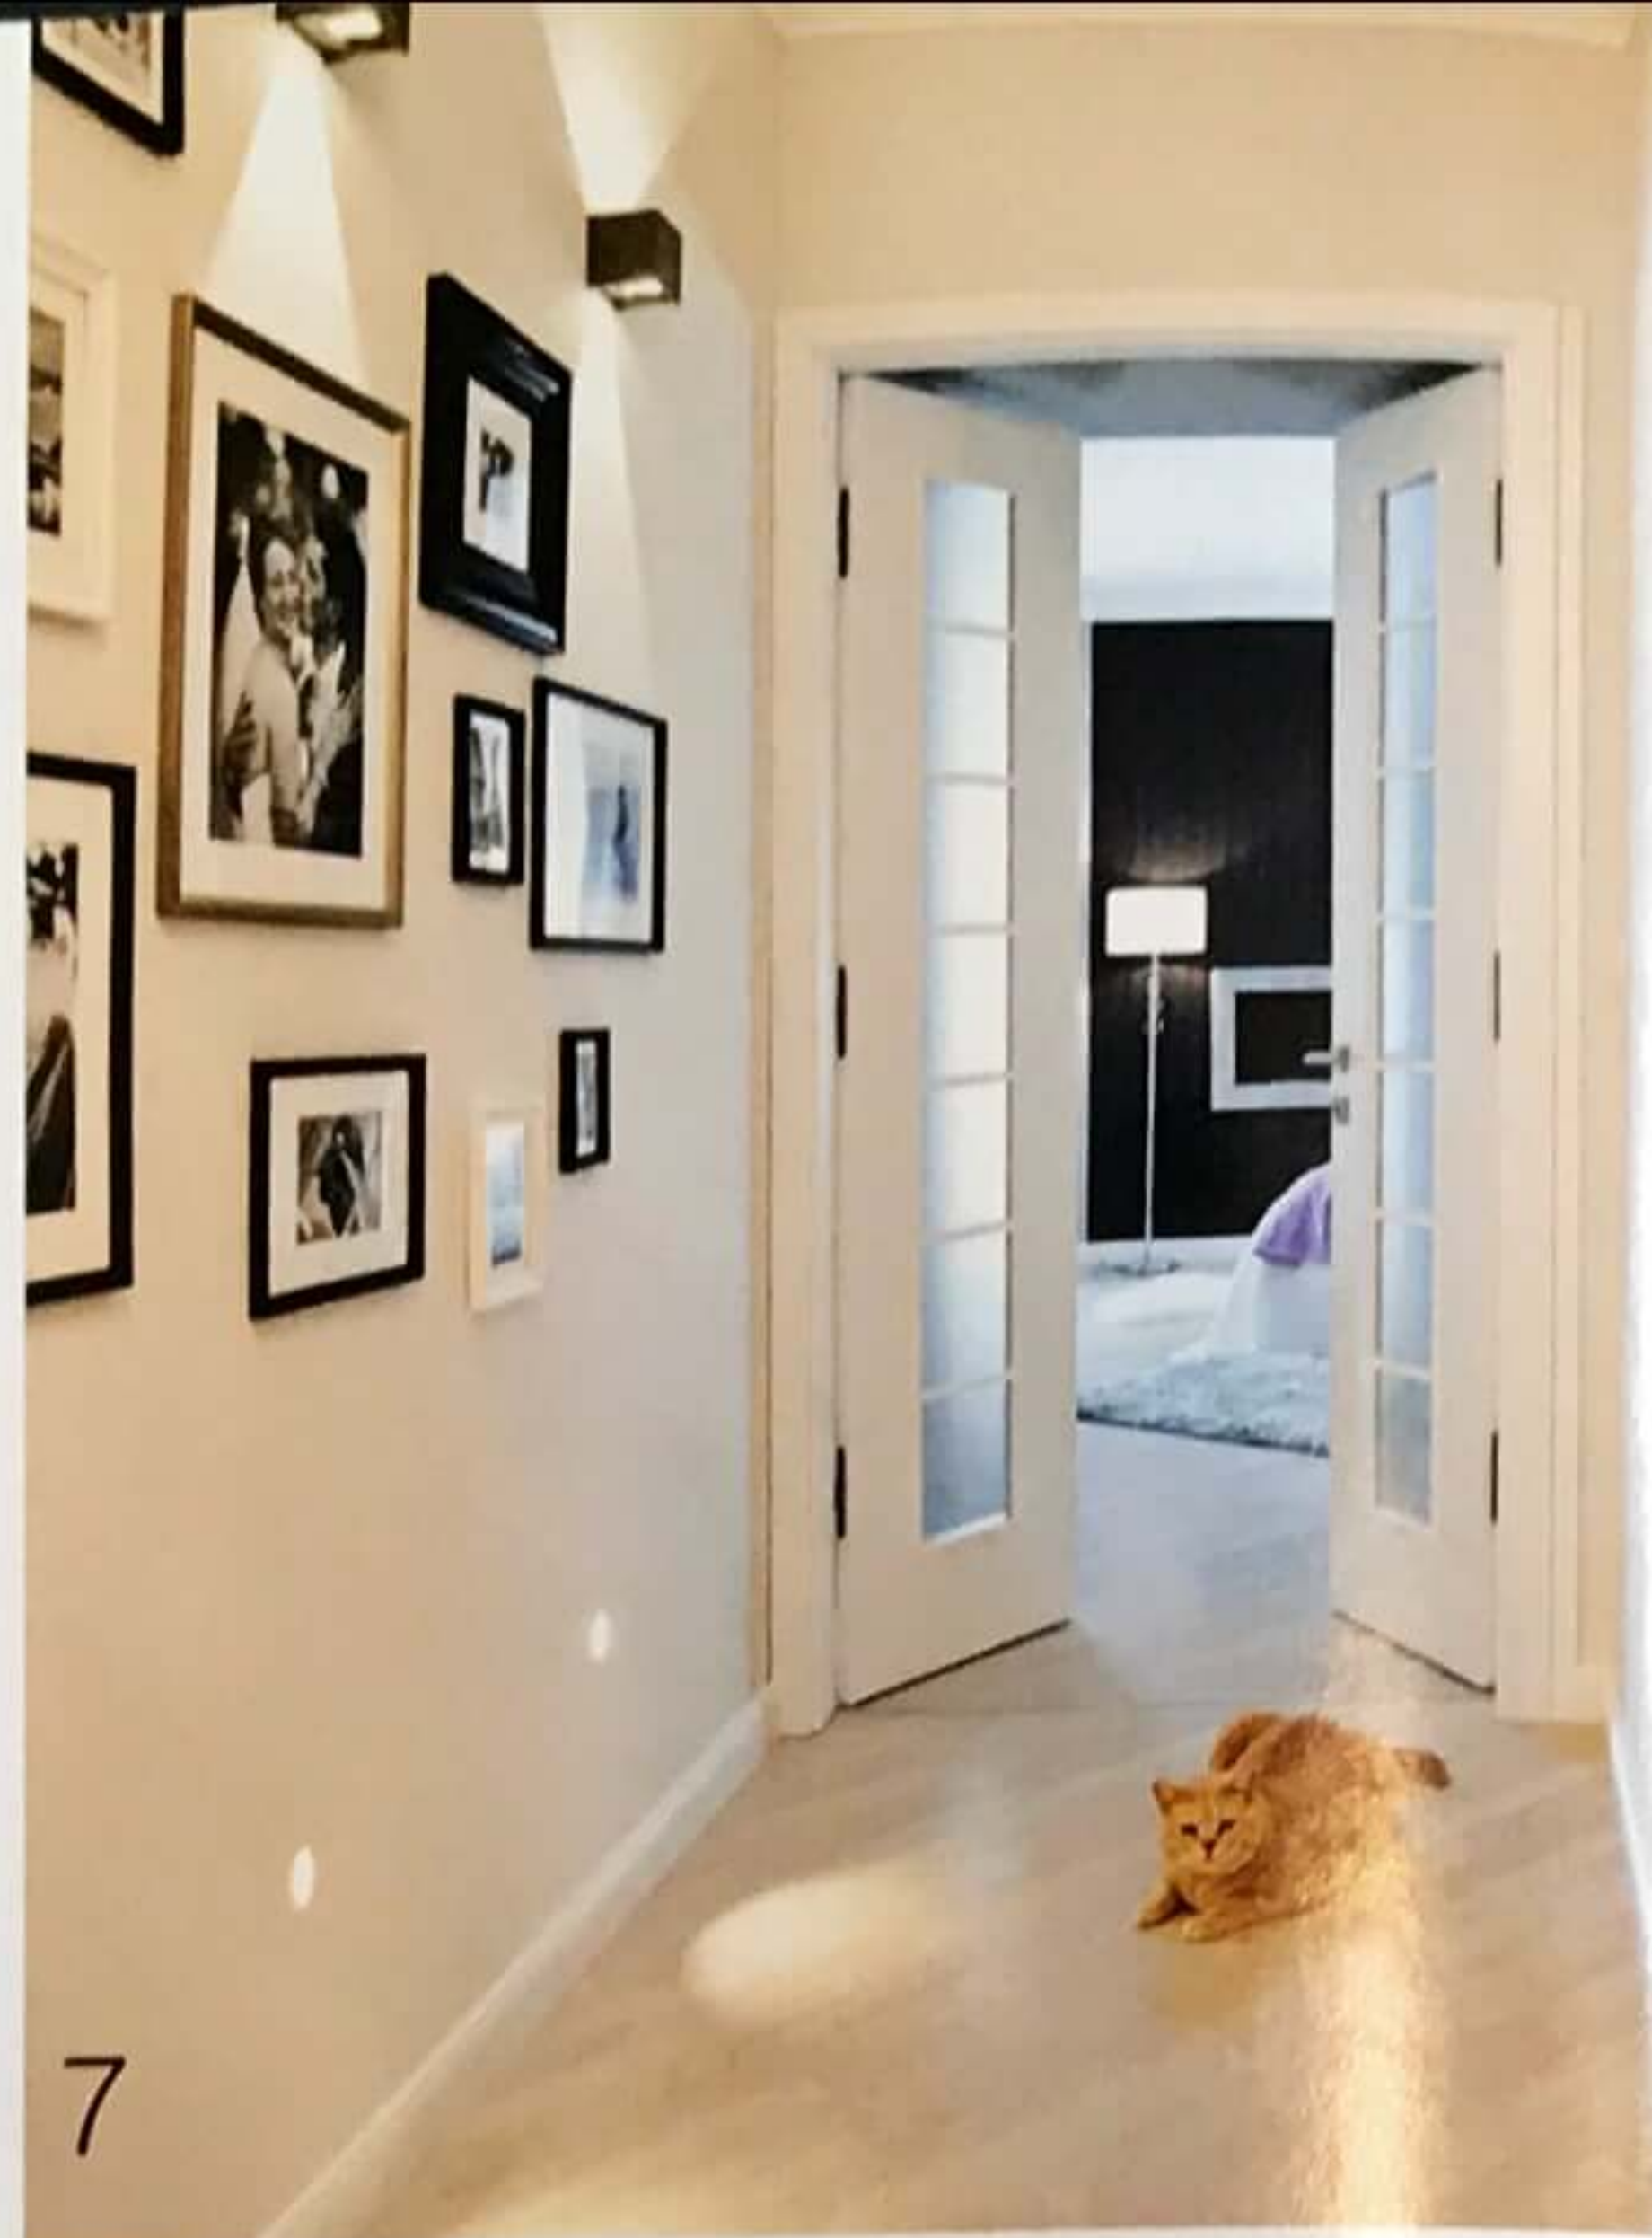

7



6

a sötétebb tónusú szürke köszön vissza a kanapé huzatában is, amelyet azóta a ház cicája vesz rendszerint birtokba. Ide a kanapé fölé élő zöldkép kompozíciót függesztettünk. A ház elbontatlan szerkezeti elemei egy beugrót képeztek, amit végül egyedi bútorkompozícióval jól ki tudtunk használni. Az azúr színek behozatalában Péli Noémi gyönyörű kerámiái is segítettek, ami mögött hasonló árnyalatú gyöngyház csillogású tapétával borítottuk a falat.

A tárolási funkciók nagy részét a hálósobában sikerült megoldani. Az egyik falat végig begardróboztuk, amit meleg szürke Matelac üveggel borított toloajtók mögé rejtettem. Az üveg felületek szigorúságát lágyítandó, az ágy mögötti falra puha, ezüstös színű textilbőrrel bevont paneleket csináltattam. Bizonyára a déli temperamentum az oka, de mind a hálósobába és meglepő módon a fürdőbe is egy-egy bioetanol kandallót kértek.

A fürdőben helyet kellett csinálnom egy szabadon álló kádnak, zuhanyzónak, de még a mosókonyhának is. Háromféle, karakterében elütő csempe teszi izgalmassá a romantikus kandallós fürdőszobát. Visszaköszön a nappali sötétszürkéje, a konyakos faszín és a fehér is, bár itt 3D-s hullámokkal kiegészülve.

A közlekedőket fényvetőkkel igyekeztem mozgalmassabbá tenni, de végül a nagyon kedves hangulatot a megrendelőim által, esküvői és családi képekből összeállított kompozíció adta.

INFOPLUSZ

Építészeti tervezés: Petyerák Katalin



5 A hagyományos zuhanyfalat tükörfelülettel megoldva nagyobb a térérzet.

6 A szabálytalan alaprajzot ellensúlyozandó választottuk ki a mosdókat és a kádat is

7 Időnként a ház egyik kedvence is elmélázik az esküvői fotók előtt. Itt a sík felületet kis fényvetőkkel törtük meg

8 Anyaghasználatban és a színekben is arra törekedtünk, hogy a hálósobában a légység domináljon. A textilbőrrel bevont panelek nem megszokott módon, a cicák által már nem elérhető helyre kerültek

8